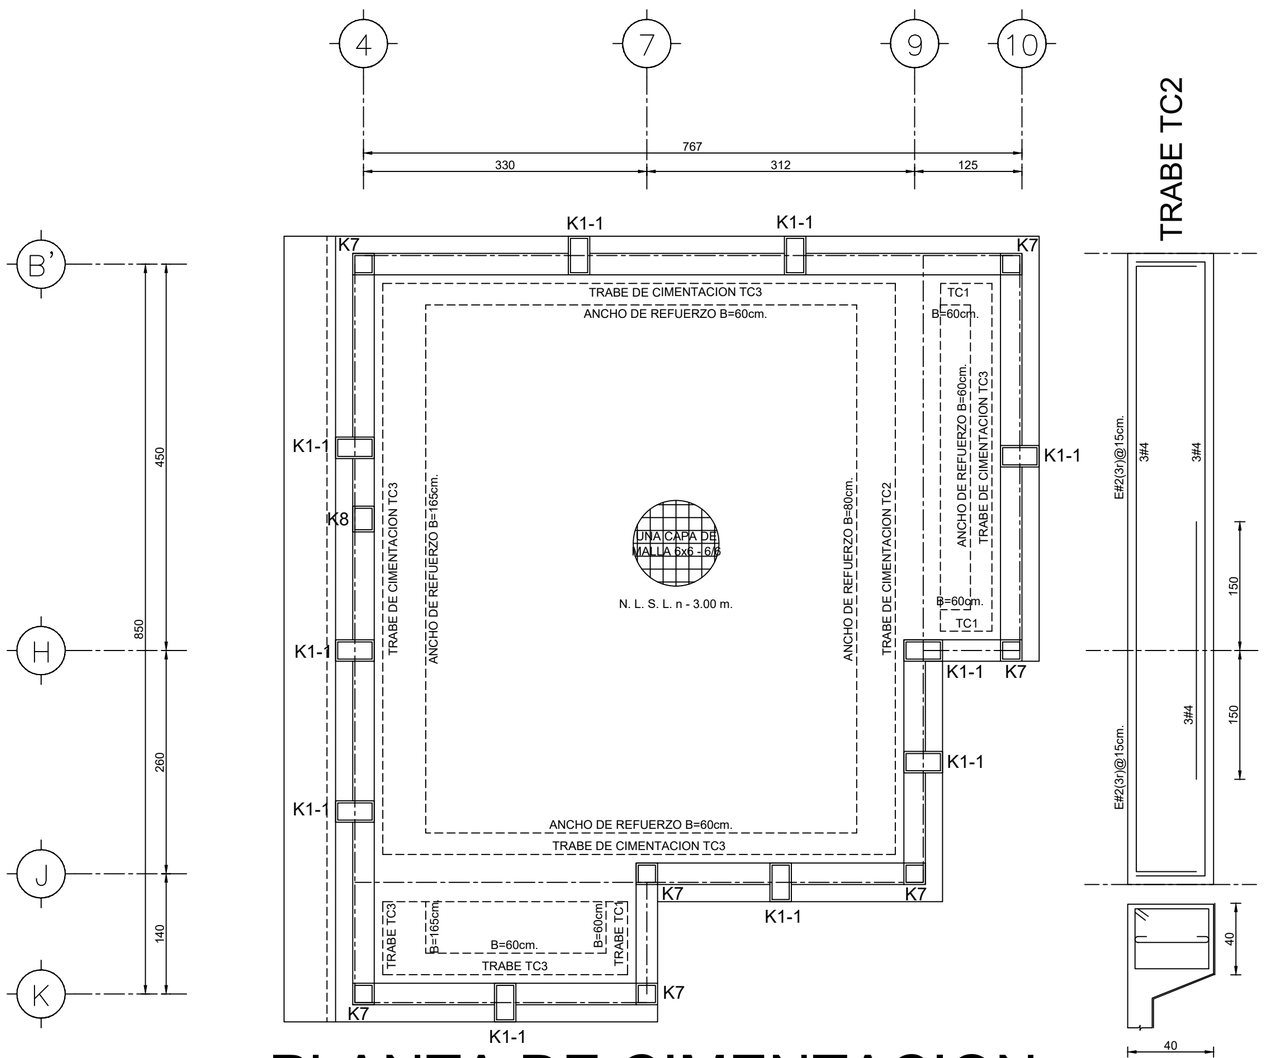

PLANTA DE CIMENTACION

RESISTENCIA DEL SUELO CONSIDERADA, R = 7.50 T/m2
LOSA DE 15 cm. DE ESPESOR.

ESCALA 1 : 50

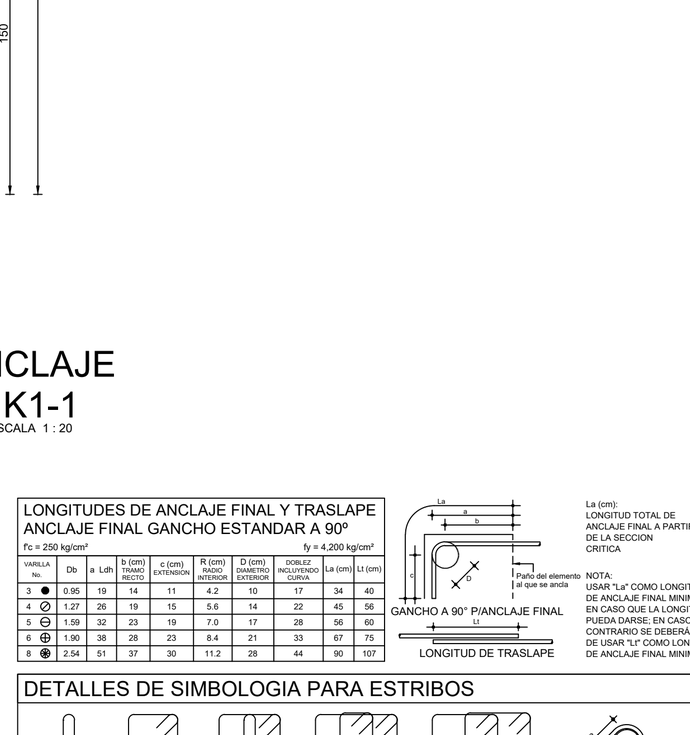

DETALLE DE MURO CONTENCION

ESCALA 1:20

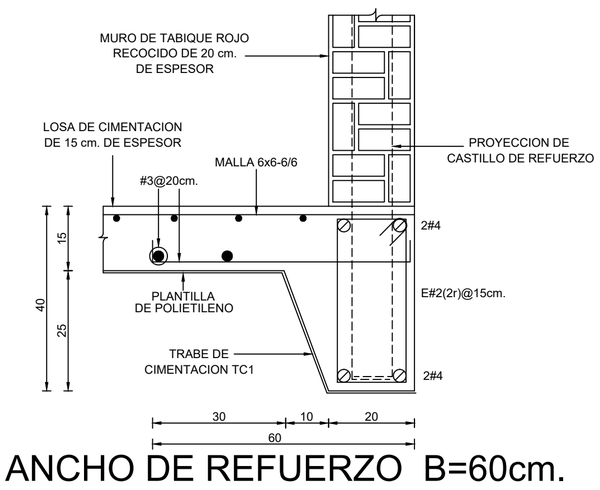

ANCHO DE REFUERZO B=60cm.

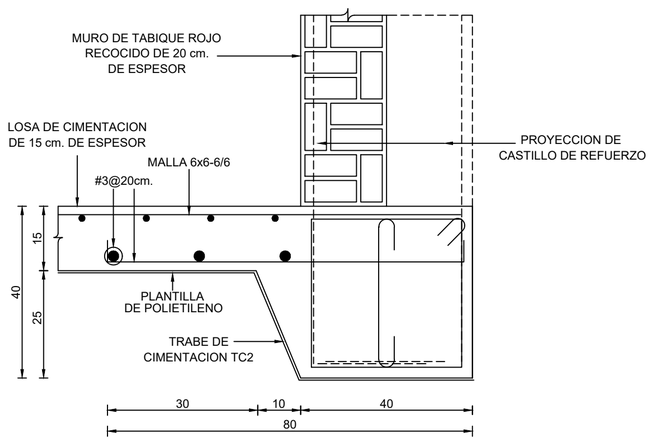

ANCHO DE REFUERZO B=80cm.

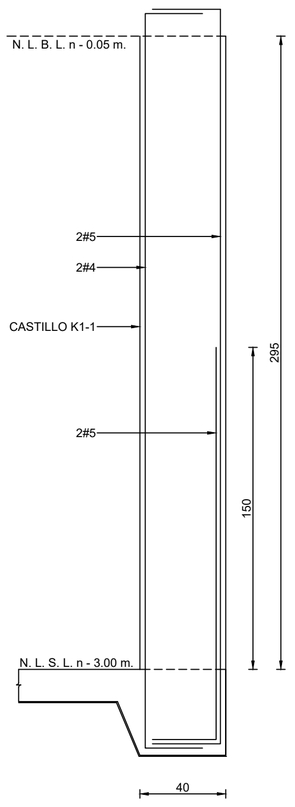

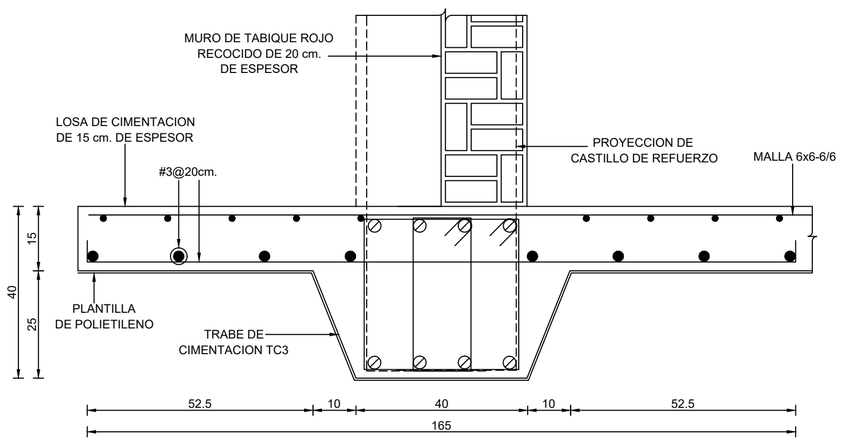

ANCHO DE REFUERZO B=165cm.

CASTILLO K1-1

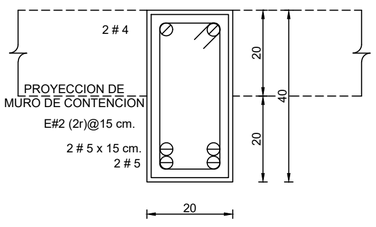

DALA DE REMATE DE MURO

ESCALA 1 : 10

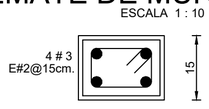

CASTILLO K7

CASTILLO K8

NOTAS Y ESPECIFICACIONES

1 CONCRETO f'c = 250 kg/cm² PARA CIMENTACION, COLUMNAS Y MCx
CONCRETO f'c = 200 kg/cm² PARA CASTILLOS Y DALAS
TODO EL CONCRETO LLEVARÁ LAS SIGUIENTES CARACTERISTICAS
AGREGADO MAXIMO DE 3/4" (19 mm .)
REVENIMIENTO DE 10 A 12 cm.
CEMENTO PORTLAND TIPO II
2 ACERO DE REFUERZO A.S.T.M. A-615 GRADO 42 (fy = 4,200 kg/cm²)
PARA TODOS LOS DIAMETROS INDICADOS
ACERO DE REFUERZO GRADO ESTRUCTURAL (fy = 2,530 kg/cm²)
PARA TODA LA VARILLA INDICADA CON EL #2 (1/4" Ø)
ACERO DE REFUERZO GRADO 50 (fy = 5,000 kg/cm²)
PARA LOS PREFABRICADOS ARMEX Y MALLA ELECTROSOLDADA
3 TODA LA CIMENTACION DEBERÁ CONSTRUIRSE SOBRE UNA PLANTILLA DE CONCRETO POBRE f'c = 100 kg/cm² DE 5 cm. DE ESPESOR EN CASO DE LOSA DE CIMENTACION, ESTA DEBE DE CONSTRUIRSE SOBRE UNA PLANTILLA DE POLIETILENO DE 400 MICRAS
4 DEBERÁ COMPACTARSE LA SUPERFICIE DE DESPLANTE ANTES DEL COLADO DE LA PLANTILLA, AL 95% DE SU P.V.S.M.
5 LAS JUNTAS FRIAS DE COLADO DEBERAN DEJARSE ENTRE CASTILLOS AL CENTRO DE LA DISTANCIA ENTRE AMBOS, SE HARÁN VERTICALES Y SE DARÁ TRATAMIENTO CON MEMBRANA DE ADHERENCIA ANTES DE CONTINUAR CON EL COLADO (VER DETALLE ADJUNTO)
6 RECUBRIMIENTO CONSIDERADO EN CIMENTACIÓN, 5 cm. LIBRES
7 LA LOCALIZACION DEL REMATE DEL ESTRIBO DE CUALQUIER ELEMENTO DEBERA ALTERNARSE DE UNO A OTRO LADO DEL MISMO
8 VER COTAS Y NIVELES GENERALES EN PLANOS ARQUITECTONICOS
9 NO TOMAR MEDIDAS A ESCALA
10 LAS COTAS RIGEN AL DIBUJO
11 TODOS LOS MUROS SERAN DE TABIQUE ROJO RECOCIDO DE 15 cm. DE ESPESOR, SE ASENTARÁN CON MORTERO TIPO II, CON RESISTENCIA NOMINAL A LA COMPRESION f*b = 75 kg/cm² (CEM-CAL-ARE 1:1:5)
12 TODOS LOS MUROS LLEVARAN CADENAS DE CERRAMIENTO A UNA DISTANCIA NO MAYOR A 3.00m. UNA DE OTRA.
PARA LOS MUROS QUE NO EXCEDAN LOS 3.00m. DE ALTURA, LA DALA SERA COLOCADA EN LA CORONA DEL MURO, DE FORMA HORIZONTAL, SIENDO SU SECCION Y ARMADO MINIMO, 20x12cm., ARMEX 12x20-4.
PARA EL CASO DE LAS PUERTAS Y VENTANAS, ESTAS LLEVARAN DALA DE CERRAMIENTO UNICAMENTE SOBRE SU VANO, SIENDO SU SECCION Y ARMADO MINIMO, 15x20cm., ARMEX 12x20-4.
13 EL ORIGINAL DE ESTE PLANO ES PROPIEDAD Y RESPONSABILIDAD EXCLUSIVA DEL CALCULISTA QUE FIRMA ESTA COPIA, CUALQUIER MODIFICACION DE SECCIONES, ARMADOS Y/O MODIFICACIONES ARQUITECTONICAS, DEBERAN SER PREVIAMENTE CONSULTADAS AL CALCULISTA, EL CUAL DARÁ SU APROBACIÓN O RECHAZO POR ESCRITO, DOCUMENTO QUE SE ANEXARA A ESTE PLANO, EN CASO DE NO SER ASÍ, EL CALCULISTA SE VERÁ LIBERADO DE TODA RESPONSABILIDAD INHERENTE A ESTE PROYECTO
14 EL CONSTRUCTOR DE LA OBRA, SERÁ EL RESPONSABLE DE LA CORRECTA INTERPRETACIÓN DEL PLANO, ASÍ COMO DE LA CALIDAD Y CARACTERÍSTICAS DE LOS MATERIALES EMPLEADOS, TANTO POR SU PERSONAL, COMO POR LOS SUBCONTRATISTAS Y DESTAJISTAS QUE INTERVENGAN EN LA EJECUCION DE LA OBRA
15 EL PROPIETARIO Y EL OCUPANTE DE LA CONSTRUCCIÓN, SERÁN LOS RESPONSABLES DEL USO DE LA MISMA, Y DE QUE LAS CARGAS VIVAS ESTIPULADAS EN LOS PLANOS NO SEAN EXCEDIDAS

CLAVE DE MUROS

- MURO DE CARGA DE 15 cm. DE ESPESOR
- MURO QUE SE DESPLANTA A PARTIR DE ESTE NIVEL
- MURO NO ESTRUCTURAL
- DALA DE CERRAMIENTO O TRABE

PROYECTO ESTRUCTURAL

analisis y diseño estructural

ING. APOLINAR CORTEZ SANCHEZ
CED. PROF. 1957836
Jose Hernandez Sierra, lote 17; col. Villa Rica, Boca del Rio, Veracruz.
tel. (229) 935 5469
apolinarcortez@hotmail.com

PROYECTO	CASA HABITACION
PROPIETARIO	ELISA SERRANO MEDINA
UBICACION	LOTE NO. 79, MANZANA. 05, BLVD. RIVIERA VERACRUZANA, 95264 FRACCIONAMIENTO EL SENDERO RESIDENCIAL, VER.
PLANO DE	CIMENTACION
FECHA	MARZO 2026
ACOTACIONES	CENTIMETROS
ESCALA	INDICADA
CLAVE DE PLANO	E-1

LONGITUDES DE ANCLAJE FINAL Y TRASLAPE
ANCLAJE FINAL GANCHO ESTANDAR A 90º

f'c = 250 kg/cm² fy = 4,200 kg/cm²

VARILLA No.	Db	a Ldh	b (cm) TRAMO RECTO	c (cm) EXTENSION	R (cm) RADIO INTERIOR	D (cm) DIAMETRO EXTERIOR	DOBLEZ INCLUYENDO CURVA	La (cm)	Lt (cm)
3 ●	0.95	19	14	11	4.2	10	17	34	40
4 ⊘	1.27	26	19	15	5.6	14	22	45	56
5 ⊖	1.59	32	23	19	7.0	17	28	56	60
6 ⊕	1.90	38	28	23	8.4	21	33	67	75
8 ⊛	2.54	51	37	30	11.2	28	44	90	107

La (cm):
LONGITUD TOTAL DE ANCLAJE FINAL A PARTIR DE LA SECCION CRITICA

NOTA:
USAR "La" COMO LONGITUD DE ANCLAJE FINAL MINIMA, EN CASO QUE LA LONGITUD "a" PUEDA DARSE; EN CASO CONTRARIO SE DEBERÁ DE USAR "Lt" COMO LONGITUD DE ANCLAJE FINAL MINIMA.

DETALLES DE SIMBOLOGIA PARA ESTRIBOS