


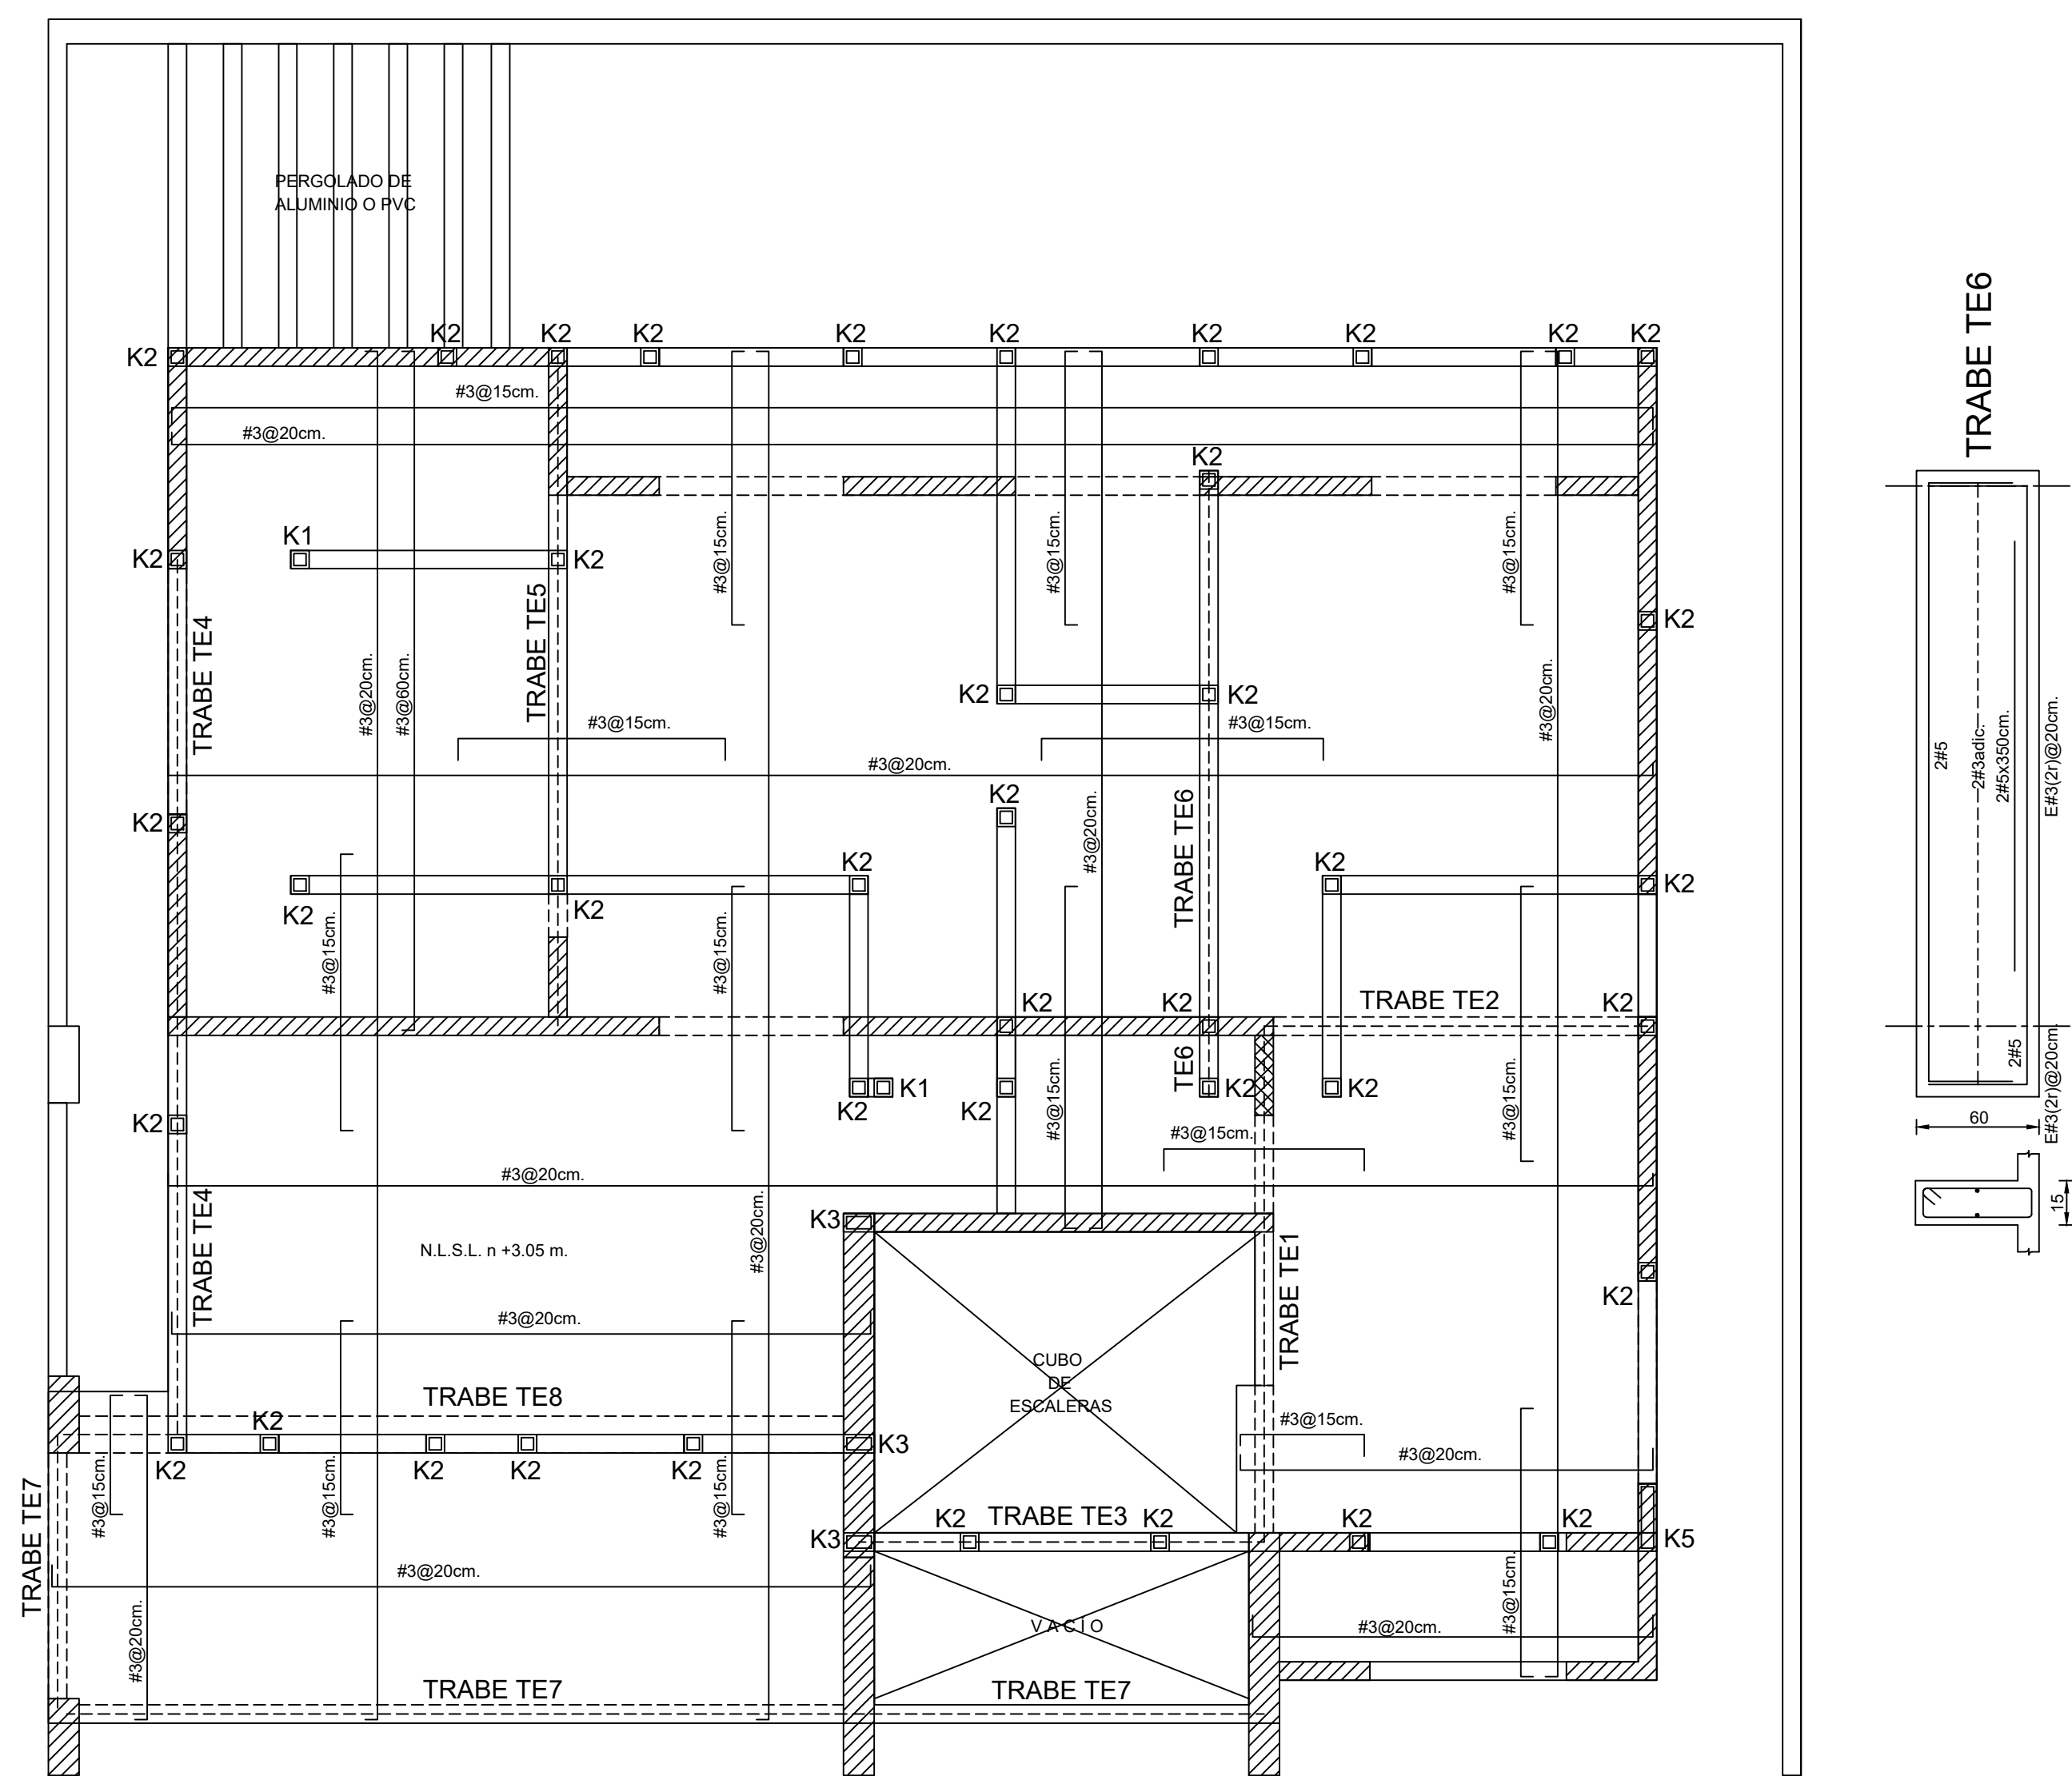

LOSA MACIZA DE 15 cm. DE ESPESOR.  
CARGA VIVA CONSIDERADA  $W_v = 190 \text{ kg/m}^2$

**TRABE TE7**  
ESCALA 1:10

75  
15  
60

2#4

4#3adic.  
E#3(2r)@20cm.

2#4

15

**TRABE TE8**  
ESCALA 1:10

75  
15  
60

4#5

4#3adic.  
E#3(4r)@20cm.

4#5x600cm.  
4#5

30

ESCALA 1:10

ARMEX  
12x20-4

20

15

SOBRE PUERTAS  
Y VENTANAS

6 # 3  
E#2@15cm.

ESCALA 1:10

20

25

SOBRE PUERTAS  
Y VENTANAS

| LONGITUDES DE ANCLAJE FINAL Y TRASLAPES |                |                   |                          |                     |                                           |                                |                              |         |         |
|-----------------------------------------|----------------|-------------------|--------------------------|---------------------|-------------------------------------------|--------------------------------|------------------------------|---------|---------|
| ANCLAJE FINAL GANCHO ESTANDAR A 90°     |                |                   |                          |                     |                                           |                                |                              |         |         |
| f <sub>c</sub> = 250 kg/cm <sup>2</sup> |                |                   |                          |                     | f <sub>y</sub> = 4,200 kg/cm <sup>2</sup> |                                |                              |         |         |
| VARIABLE                                | D <sub>b</sub> | A Ld <sub>t</sub> | D (cm)<br>TRANS<br>RECTO | c (cm)<br>EXTENSION | R (cm)<br>RADIO<br>INTERIOR               | D (cm)<br>DIAMETRO<br>EXTERIOR | DOBLEZ<br>INCLINADO<br>CURVA | La (cm) | Li (cm) |
| 3 ●                                     | 0.95           | 19                | 14                       | 11                  | 4.2                                       | 10                             | 17                           | 34      | 40      |
| 4 ○                                     | 1.27           | 26                | 19                       | 15                  | 5.6                                       | 14                             | 22                           | 45      | 56      |
| 5 ⊕                                     | 1.59           | 32                | 23                       | 19                  | 7.0                                       | 17                             | 28                           | 56      | 60      |
| 6 ⊕                                     | 1.90           | 38                | 28                       | 23                  | 8.4                                       | 21                             | 33                           | 67      | 75      |
| 8 ⊕                                     | 2.54           | 51                | 37                       | 30                  | 11.2                                      | 28                             | 44                           | 90      | 107     |

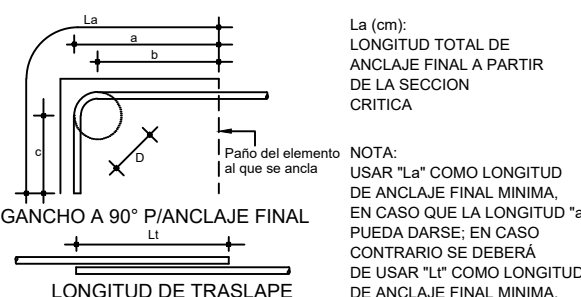
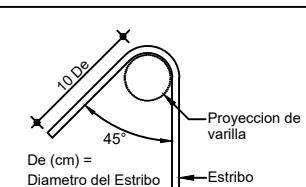


Diagrama de los tipos de estribo de una a cuatro ramas:

- ESTRIBO DE UNA RAMA (1)
- ESTRIBO DE DOS RAMAS (2)
- ESTRIBO DE TRES RAMAS (3)
- ESTRIBO DE CUATRO RAMAS (4a)
- ESTRIBO DE CUATRO RAMAS (4b)

[illegible]

E-4