


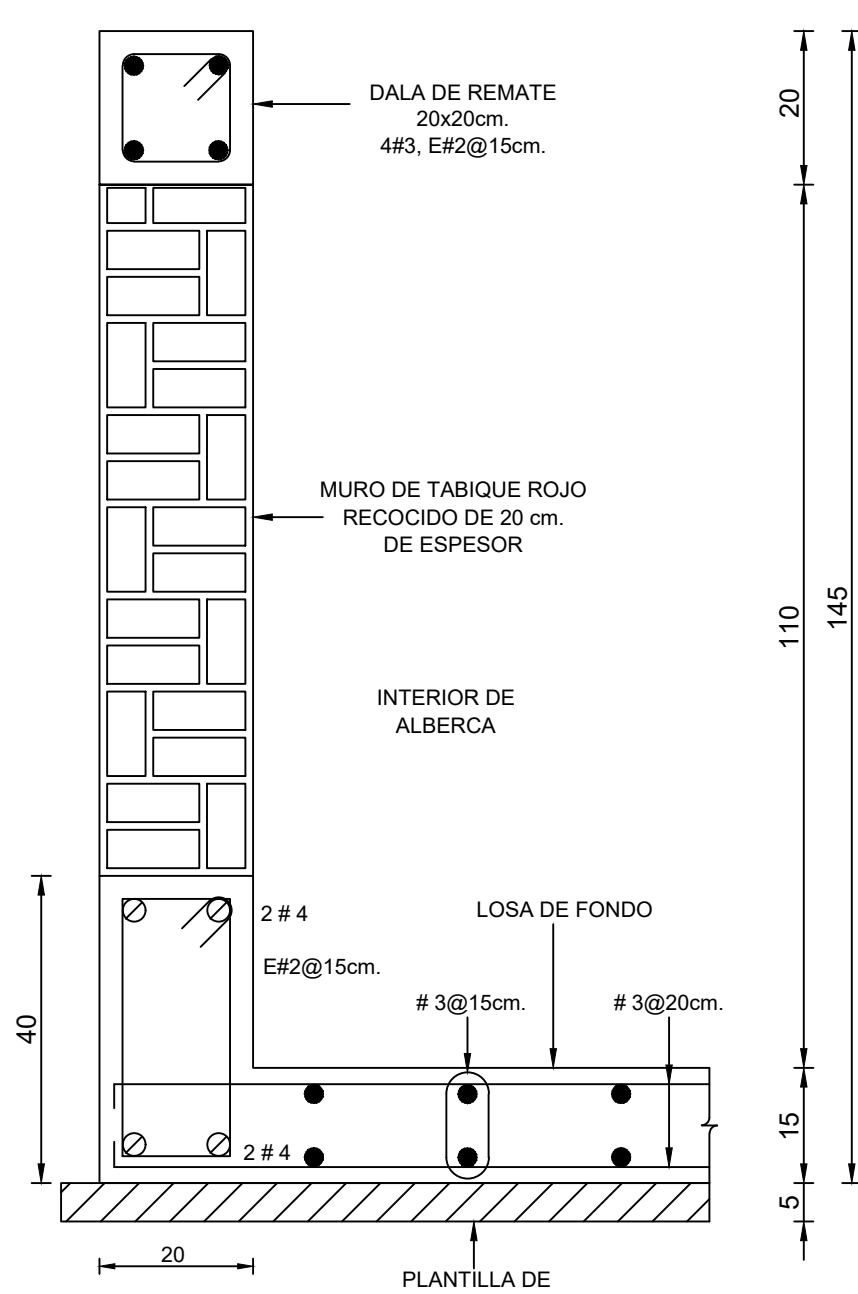
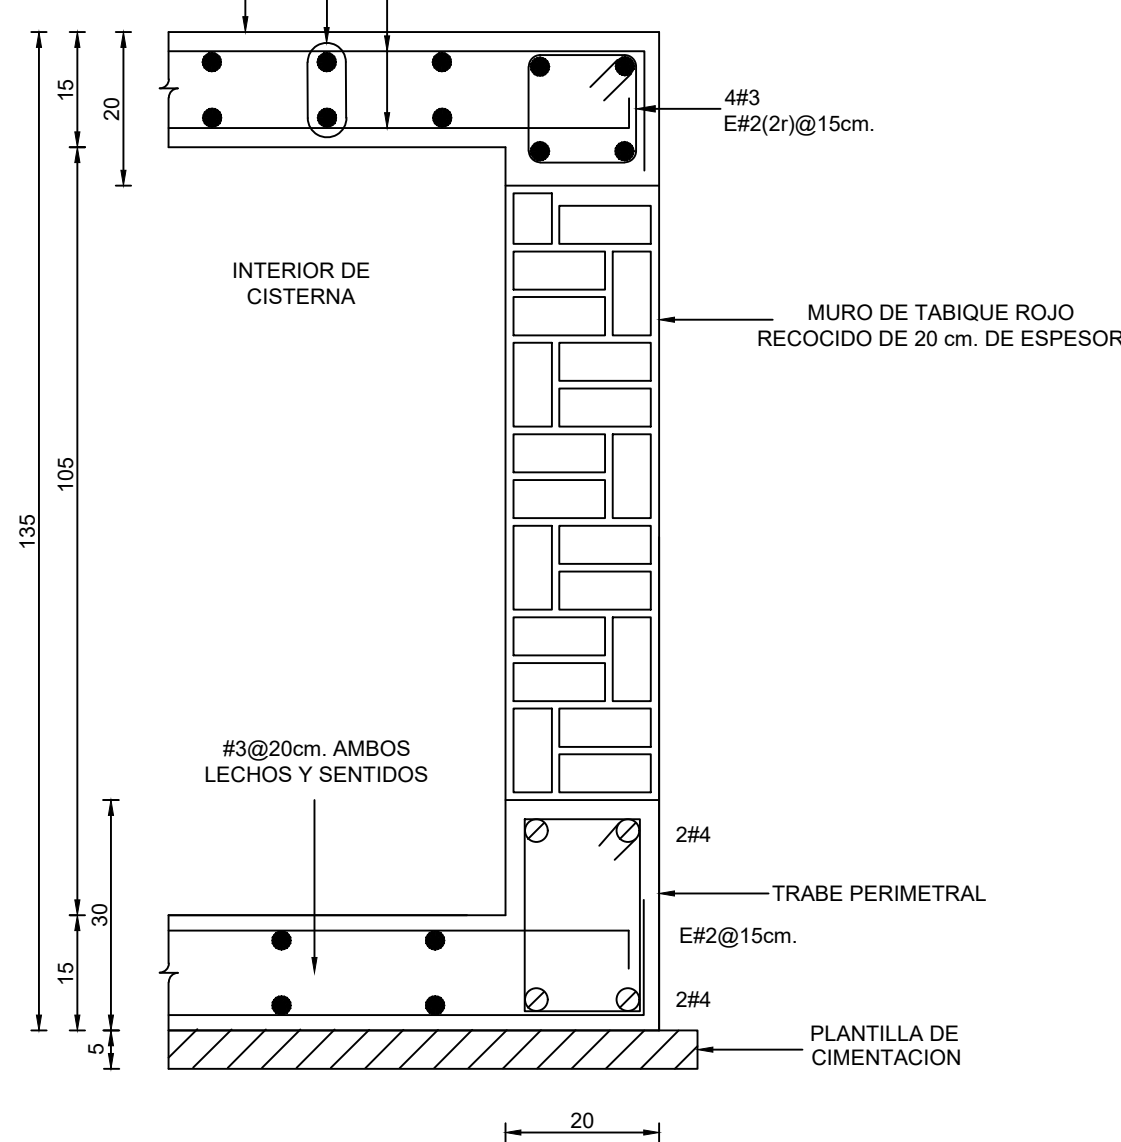
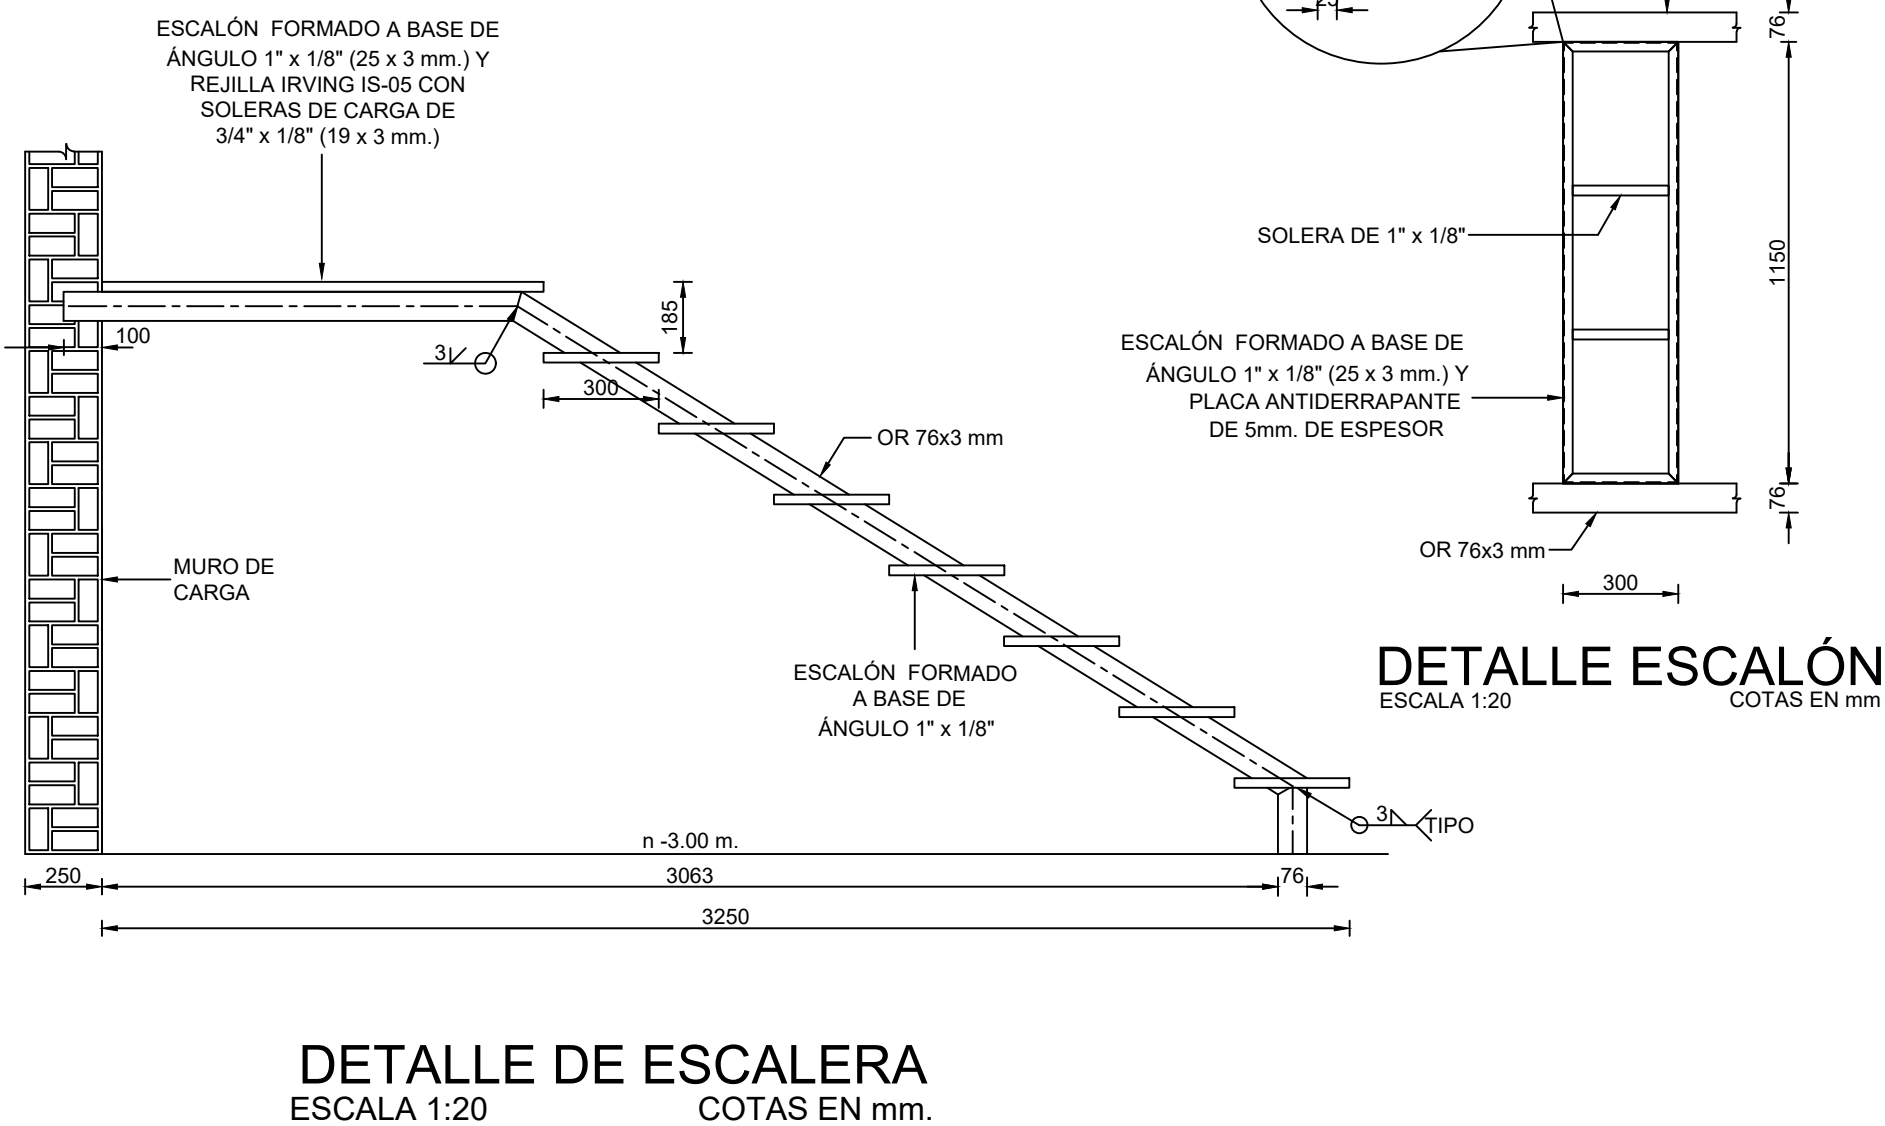
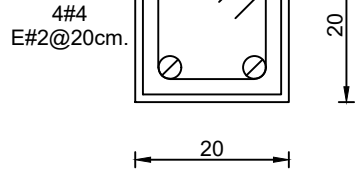
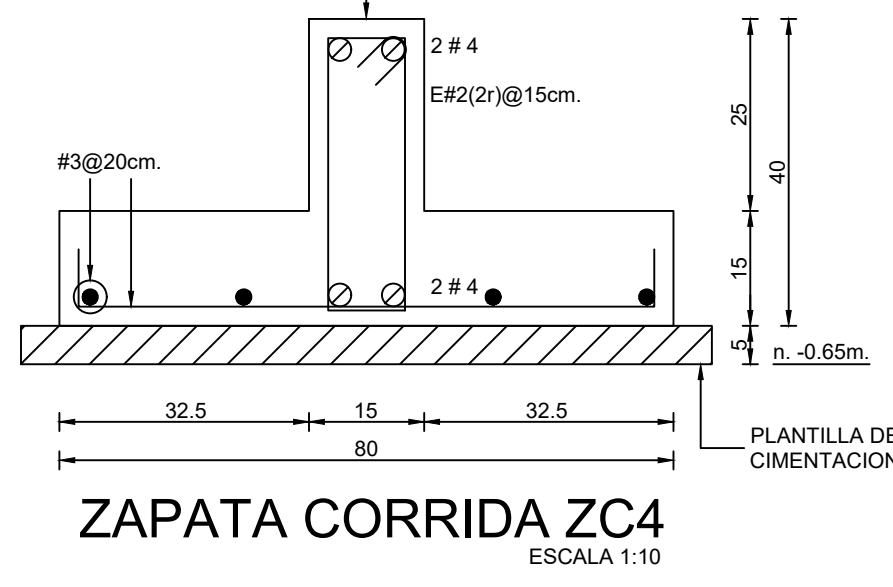
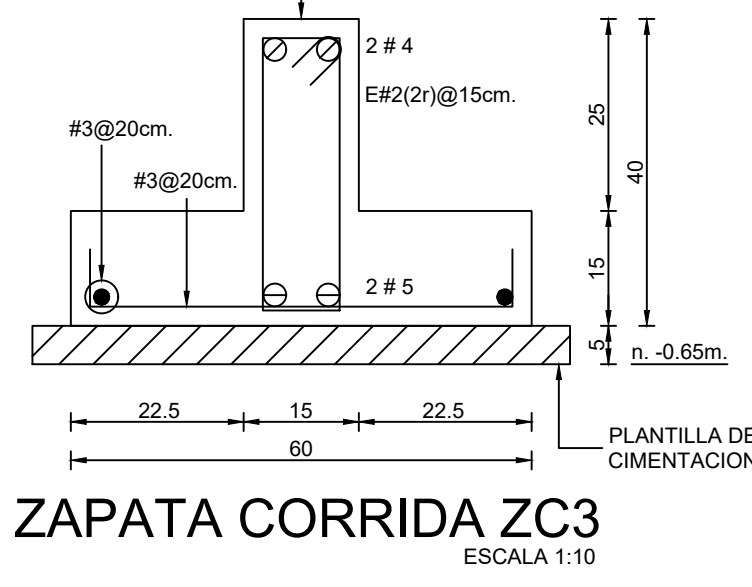
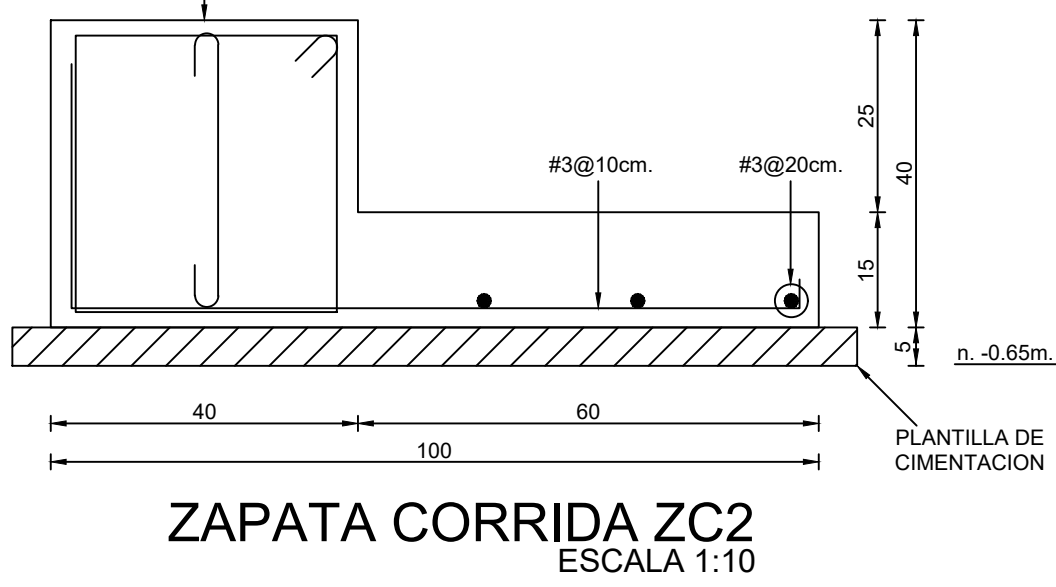
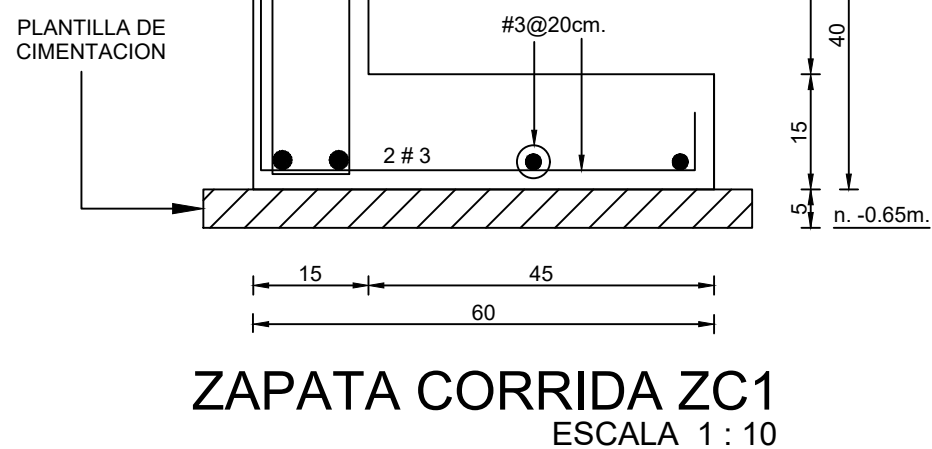
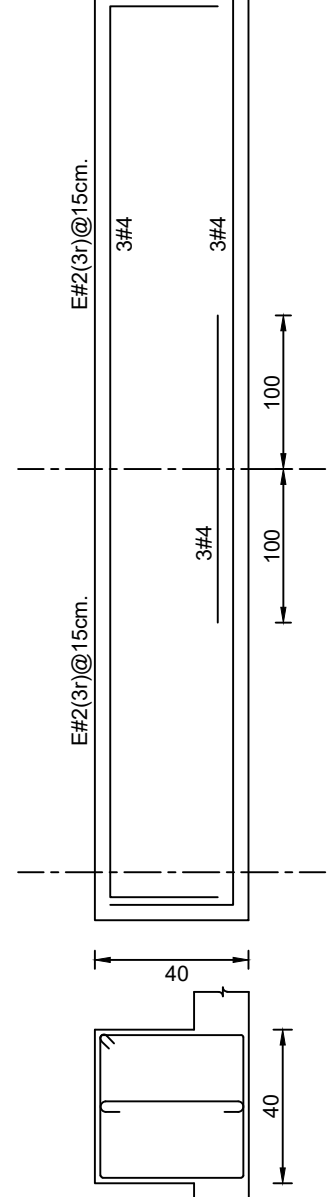
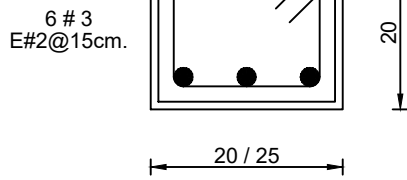


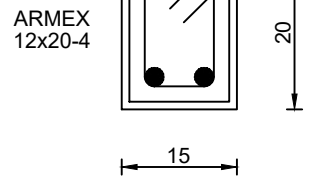

LONGITUDES DE ANCLAJE FINAL Y TRASLAPES ANCLAJE FINAL GANCHO ESTANDAR A 90°									
fc = 250 kg/cm²					fy = 4.200 kg/cm²				
VARIABLE	Ob	a Ldh	b (cm) TRAMO RECTO	c (cm) EXTENSION	d (cm) RABO INTERIOR	e (cm) DIAMETRO EXTERIOR	CONCL. INCLUYENDO CURVA	La (cm)	Li (m)
3 ●	0,95	19	14	11	4,2	10	17	34	4
4 ⊘	1,27	26	19	15	5,6	14	22	45	5
5 ⊖	1,59	32	23	19	7,0	17	28	56	6
6 ⊕	1,90	38	28	23	8,4	21	33	67	7
8 ⊗	2,54	51	37	30	11,2	28	44	90	10

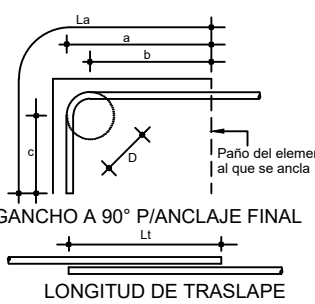

DETALLES DE SIMBOLOGIA PARA ESTRIBOS

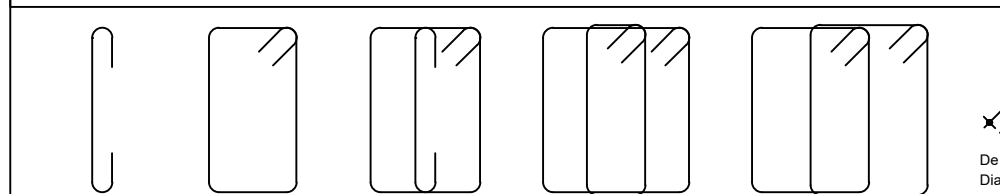

CONCRETO $f_c = 250$ kg/cm² PARA CIMENTACION, COLUMNS Y MCK
CONCRETO $f_c = 200$ kg/cm² PARA CASTILLOS Y DALAS
TODO EL CONCRETO LEVANTA LAS SIGUIENTES CARACTERISTICAS
REQUERIDAS PARA EL DISEÑO DE 19 cm.
REVENIMIENTO DE 10 A 12 cm
CEMENTO PORTLAND TIPO II
100 kg/m² (220 lb) PARA CIMENTACION, A15 GRADO 42 ($f_c = 4,200$ kg/cm²)
PARA TODOS LOS DIAMETROS
ACERO DE REFUERZO GRADO 60 ESTRUCTURAL ($f_y = 2,530$ kg/cm²)
ACERO DE REFUERZO GRADO 55 MALLA ELECTRODOSADA
3.00 mm (1/8") PARA CIMENTACION, A15 GRADO 42 ($f_c = 4,200$ kg/cm²)
ACERO DE REFUERZO GRADO 50 ($f_y = 5,000$ kg/cm²)
PARA LOS PREFABRICADOS ARMY Y MALLA ELECTRODOSADA
3.00 mm (1/8") PARA CIMENTACION, A15 GRADO 42 ($f_c = 4,200$ kg/cm²)
ACERO DE REFUERZO GRADO 50 ($f_y = 5,000$ kg/cm²)
PARA LOS PREFABRICADOS PORRE Y 100 kg/cm² DE 5 mm. DE ESPESOR
EN CASO DE LONA DE CEMENTACION, ESTA DEBE DE CONSTRUISE
SUSCRO UNA PANTALLA DE POLIETILENO DE 40 MICRAS
DE ESPESOR PARA PROTEGER LA LONA DE CEMENTACION ANTES DEL
COLADO DE LA PANTALLA AL 95% DE SUP Y 5%
LAS JUNTAS FRIAS DE COLADO DEBEN DE DEJARSE ENTRE CASTILLOS
Y DALAS PARA EVITAR EL AGUJEREO EN LAS JUNTAS

SE DA TRATAMIENTO CON MEMBRANA DE ADHERENCIA ANTES DE CONTINUAR CON EL COLADO (VER DETALLE ADJUNTO)

RECURRIMIENTO CONSIDERADO EN CIMENTACIÓN: 5 cm. LÍBRAS

LA CIMENTACIÓN REQUIERE UN TRATAMIENTO CON EL MISMO ELEMENTO DEBERÁ ALTERNARSE DE UNO A OTRO LADO DEL MISMO

VER COTAS Y NIVELES GENERALES EN PLANOS ARQUITECTONICOS

VER DETALLE DE CIMENTACIÓN

LAS COTAS RIGEN EL DIBUJO

1 TODOS LOS MUROS SERÁN DE TABIQUE RJO. RECOMENDADO DE 15 cm. DE ESPESOR, SE CIMENTARÁN CON MORTERO TIPO, CON CIMENTACIÓN NOMINAL A LA COMPRESIÓN $P = 75 \text{ kg/cm}^2$ (C.C.O.-C.A.R. 1-1.5)

2 TODOS LOS MUROS LLEVARÁN CANTAS DE CERRAMIENTO A UNA DISTANCIA DE 15 CM. ENTRE SI

3 PARA LOS MUROS QUE NO EXCEDAN LOS 3.00m. DE ALTURA, LA DADA SERÁ COLOCADA EN LA CORONA DEL MUR, DE FORMA HORIZONTAL, SIENDO SU SECCIÓN Y ARMADO MÍNIMO: 20x20cm. ARMADO: 12x20-4

4 PARA LOS MUROS QUE EXCEDAN LAS 3.00m. DE ALTURA, LA DADA DE CERRAMIENTO ÚNICAMENTE SOBIRE SU SECCION, SIENDO SU SECCION Y ARMADO MÍNIMO: 15x20cm. ARMADO: 12x20-4

- 13 EL ORIGINAL DE ESTE PLANO ES PROPIEDAD Y RESPONSABILIDAD EXCLUSIVA DEL CALLISTA QUE FIRMA ESTO CUAL, CUALQUIER MODIFICACION DE SECCIONES, ARMADOS Y/O MODIFICACIONES ARQUITECTONICAS, DEBERAN SER PREVIAMENTE CONSULTADAS A CALLISTA, EL CUAL DARÁ SU APROBACION O RECHAZO POR ESTO, DOCUMENTO QUE SE ANEXARÁ A ESTE PLANO, EN CASO DE NO SER ASÍ, EL CALLISTA SE VERÁ LIBERADO DE TODA RESPONSABILIDAD INHERENTE A ESTE PROYECTO
- 14 EL CONSTRUCTOR DE LA OBRA, SERÁ EL RESPONSABLE DE LA CORRECTA INTERPRETACION DEL PLANO, ASÍ COMO DE LA CALIDAD Y CARACTERISTICAS DE LOS MATERIALES EMPLEADOS, TANTO PO SU PERSONAL, COMO POR LOS SUBCONTRATISTAS Y DESTAJISTAS QUE INTERVIENEN EN LA EJECUCION DE LA OBRA
- 15 EL CALLISTA NO SE RESPONSABILIZA DE LA CONFORMACION, SERÁN EL RESPONSABLES DEL USO DE LA MISMA, Y DE QUE LAS CARGAS VY ESTIPULADAS EN LOS PLANOS NO SEAN EXCEDIDAS

CLAVE DE MUROS

	MURO DE CARGA DE 15 cm. DE ESPESOR
	MURO QUE SE DESPLANTA A PARTIR DE E
	MURO NO ESTRUCTURAL
	DALA DE CERRAMIENTO O TRABE

PROYECTO ESTRUCTURAL

análisis y diseño estructural

cpe

ING. APOLINAR CORTEZ SANCHEZ
CEO - PCEC - 1601018

José Hernández Sierra, sala 17; cat. Vilo Rica, Boca del Río, Veracruz
tel. (229) 835 5489 apolinarcortez@cebol.com.mx

PROYECTO
CASA HABITACION
PROPIETARIO
ELISA SERRANO MEDINA
UBICACION
LOTE NO. 79, MANZANA. VERACRUZANA, 95264 FI EL SENDERO RESIDENCIAL

PLANO DE
CIMENTACION

FECHA
MARZO 2026

ACOTACIONES
CENTIMETROS

ESCALA
INDICADA

CLAVE DE PLANO

E-2